NOTAS DE CORTES

1. COTAS Y NIVELES EN METROS; NIVELES REFERIDOS AL N.P.T. DE PLANTA BAJA (±0.00).
2. ENTREPISO: LOSA ALIGERADA DE CASETONES 60×60×20 CON NERVADURAS DE 10 cm Y CAPA DE 5 cm (h = 0.25); MACIZADA EN APOYOS.
3. AZOTEA: LOSA ALIGERADA RETICULAR, MISMO SISTEMA QUE EL ENTREPISO (PERALTE FINAL SEGÚN CÁLCULO ESTRUCTURAL). SOBRE EL VACÍO: VIGAS DE CONCRETO 15×40 @ 0.75 CON CRISTAL TEMPLADO.
4. ALTURAS PROPUESTAS: ENTREPISO 3.00; PUERTAS 2.10; VENTANAS 0.90 A 2.10; PRETIL AZOTEA 0.60; PRETIL TERRAZAS 1.00.
5. PUERTAS: EL VANO INCLUYE EL ESPESOR DE LA HOJA (EJ. PUERTA DE 0.75 = HOJA 0.70 + 0.05).
6. ESCALERA CURVA SIN EL PRIMER ESCALÓN ORIGINAL: 17 PERALTES DE 0.1765 Y 16 HUELLAS EN U: 5 RECTAS DE 0.29 + 11 RADIALES DE 0.264 EN LÍNEA DE HUELLA (MÍN. 0.25). VER LÁMINA A-03.
7. FIGURAS HUMANAS, VEGETACIÓN, VEHÍCULOS Y MOBILIARIO: REFERENCIA DE SCALA.

SIMBOLOGÍA

- MURO CORTADO
- CONCRETO CORTADO (LOSA, NERVADURA, TRABE, ESCALERA)
- CASETÓN DE POLIESTIRENO
- MURO DE PIEDRA (VISTO)
- TERRENO NATURAL / RELLENO

REVISIONES
R1.5 SEP-2026 EMISIÓN ANTERIOR.
R1.6 OCT-2026 COMEDOR PARA 15 PERSONAS; ESCALERA SIN EL PRIMER ESCALÓN (17 PERALTES, HUELLAS EN U); EJES H Y 10 A CENTRO DE MURO; MURO, PUERTA Y MUEBLE EN RECÁMARA PRINCIPAL; BLOQUES DE AUTOS Y SALA; COTAS Y NOTAS SIN ENCIMARSE; DIBUJOS AMPLIADOS EN LÁMINAS.
R1.7 OCT-2026 BAÑO JUNTO A LA ALBERCA (COPIA DEL BAÑO DE ACCESO) CON LOS MUEBLES AL MURO DEL LADO DE LA ALBERCA; MURO DE RECÁMARA ALARGADO; CAMASTROS REUBICADOS.

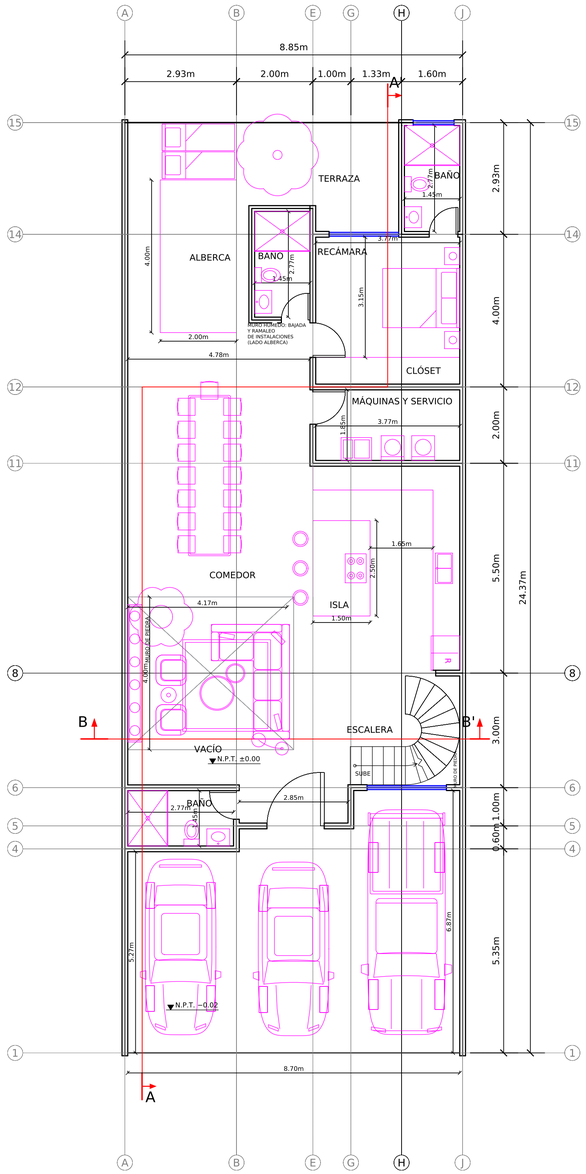

PLANTA BAJA

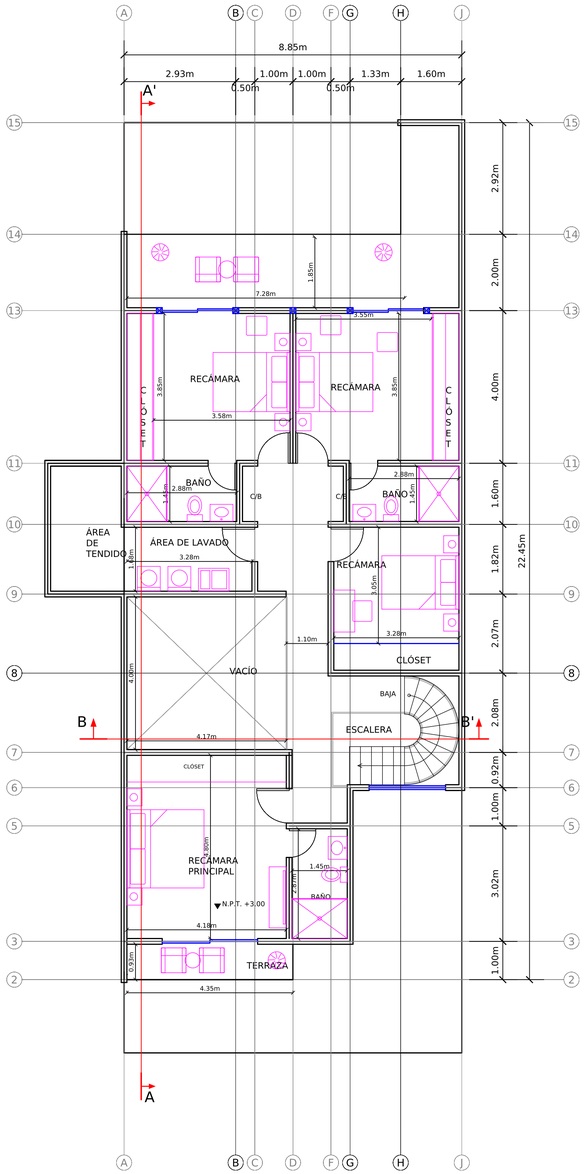

PLANTA PRIMER NIVEL

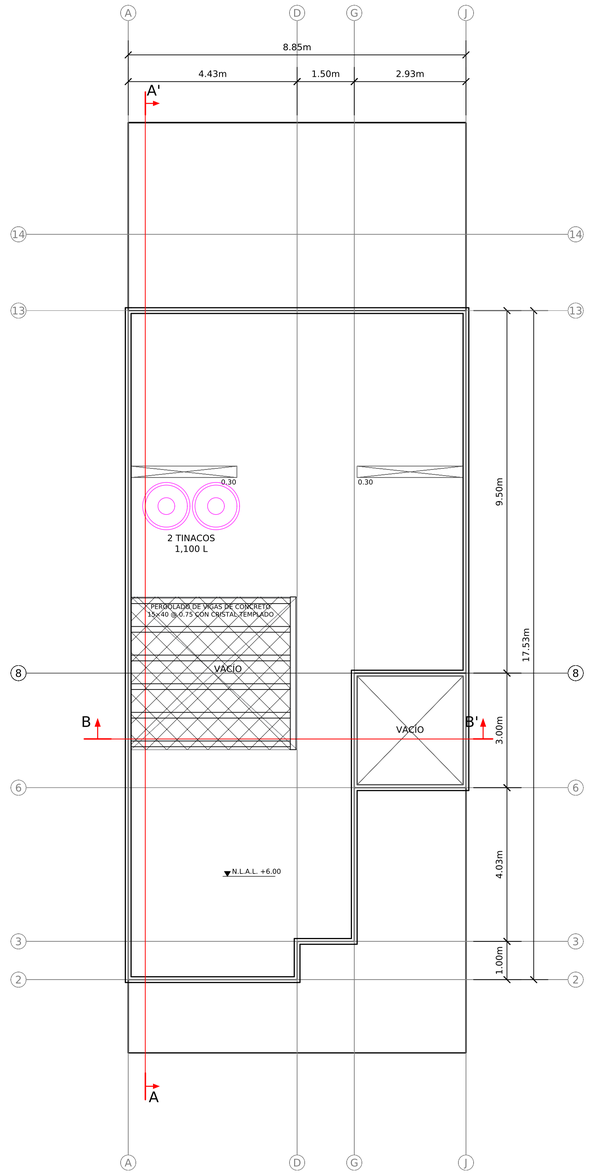

PLANTA DE AZOTEA

CASA HABITACIÓN «CROCHA»	
PLANTAS ARQUITECTÓNICAS	
ESCALA: 1:75 / NOTAS 1:50	ACOTACIONES: METROS
FECHA: OCTUBRE 2026 DIBUJÓ: ARCHIVO: 001_PLANO_CROCHA_R1.7.dxf	CLAVE: A-01 REVISÓ:

CASA HABITACIÓN «CROCHA» — R1.7: BAÑO NUEVO JUNTO A LA ALBERCA

Planta baja, acercamiento (sin escala). Cotas en metros.

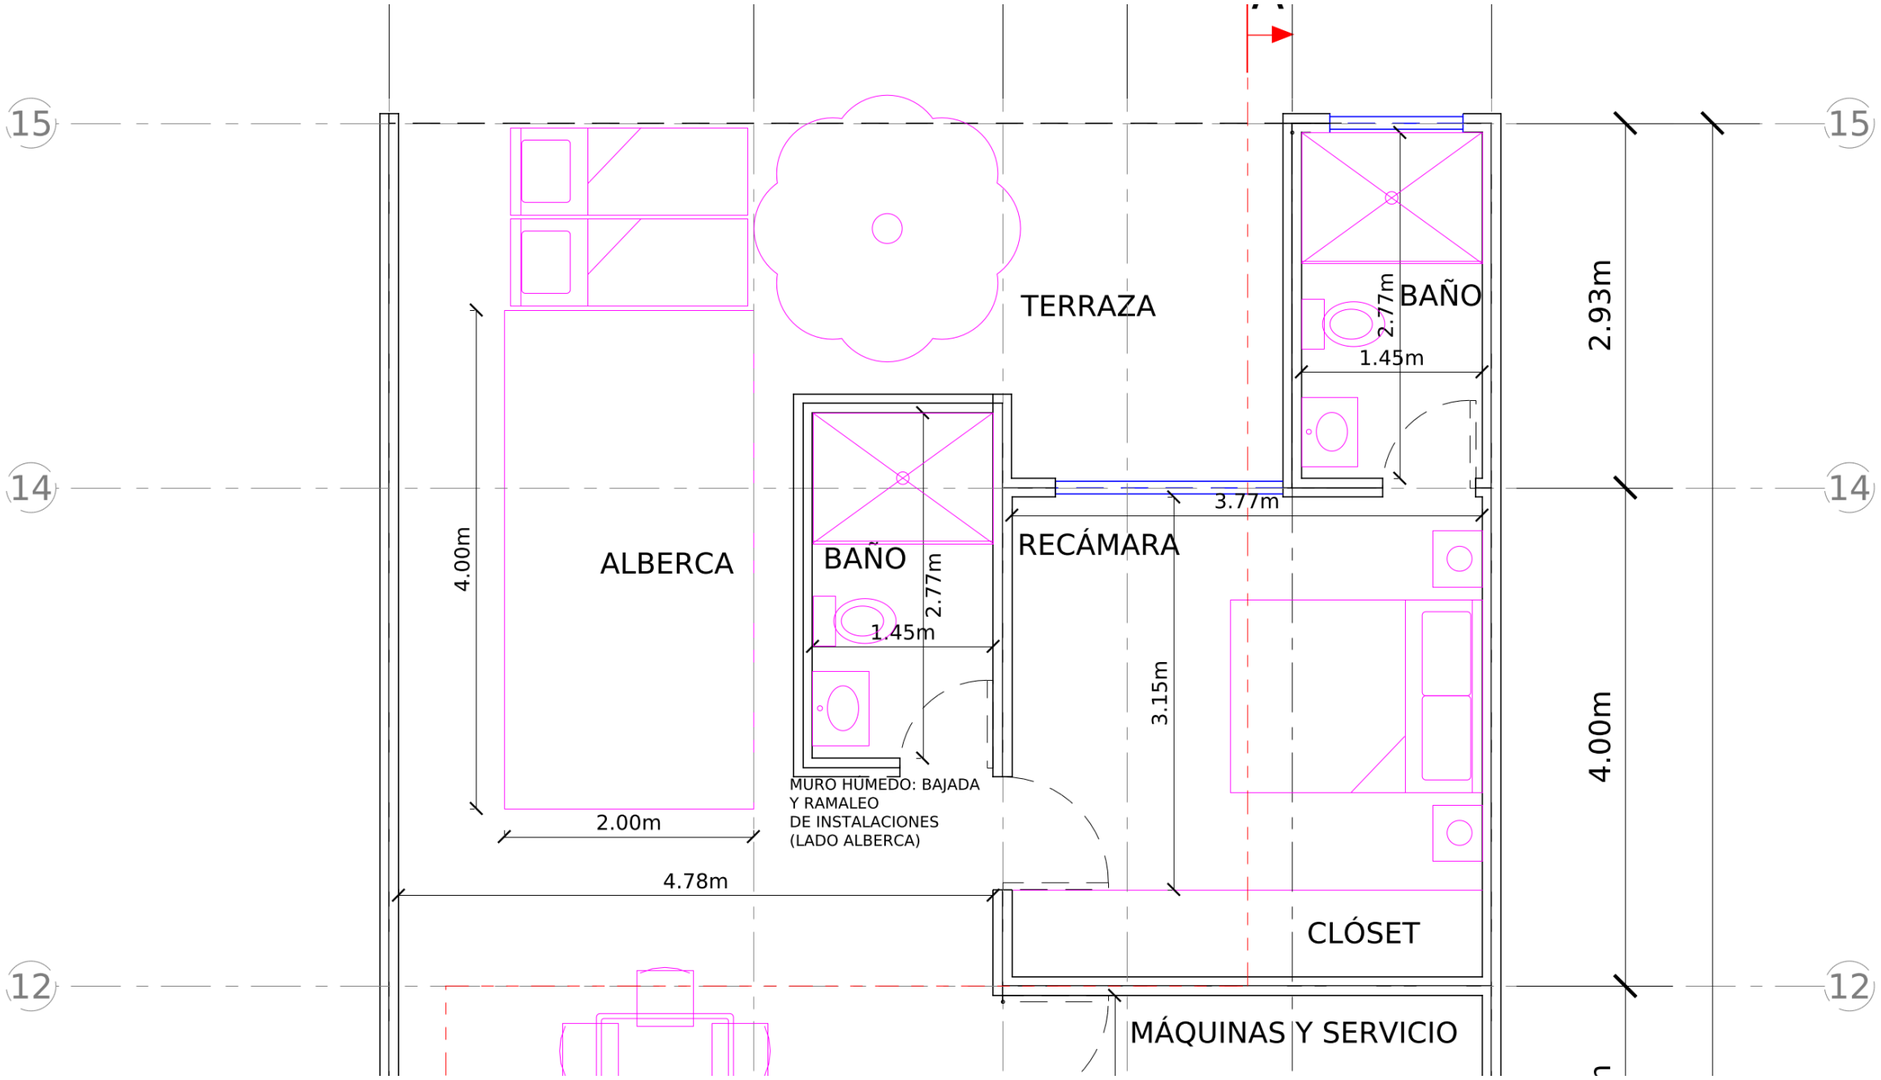

- Copia del baño de acceso (2.77 × 1.45 m interior), girado para que regadera, WC y lavabo queden en el muro del lado de la alberca (muro húmedo): por ese muro baja la instalación y se ramalea ahí mismo, sin cruzar al otro muro.
- El muro poniente de la recámara se alarga 0.68 m (del eje 14 hacia el jardín) para cerrar el baño. La puerta del baño abre junto a la de la recámara.
- Entre la alberca y el muro húmedo quedan 0.33 m para el muro de la alberca. Los camastros se pasaron al norte de la alberca y la cota de 2.00 m al lado sur.
- Ojo: los 0.75 m del baño que salen del eje 14 no quedan bajo la losa del balcón del primer nivel; llevan losa propia o se prolonga la del balcón.