

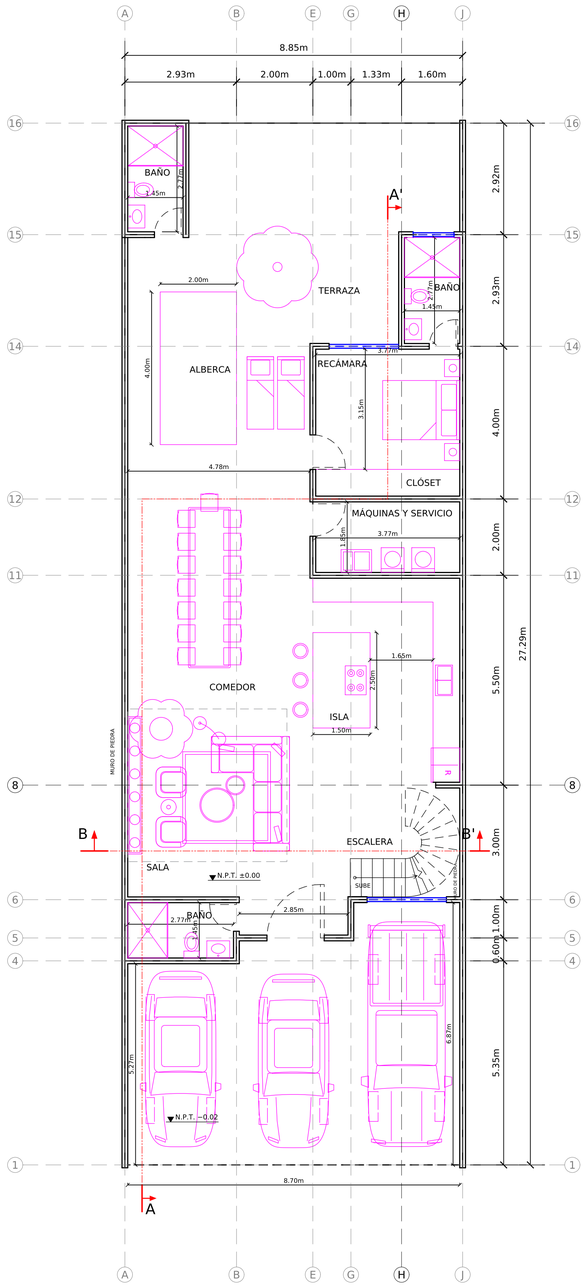


PLANTA BAJA

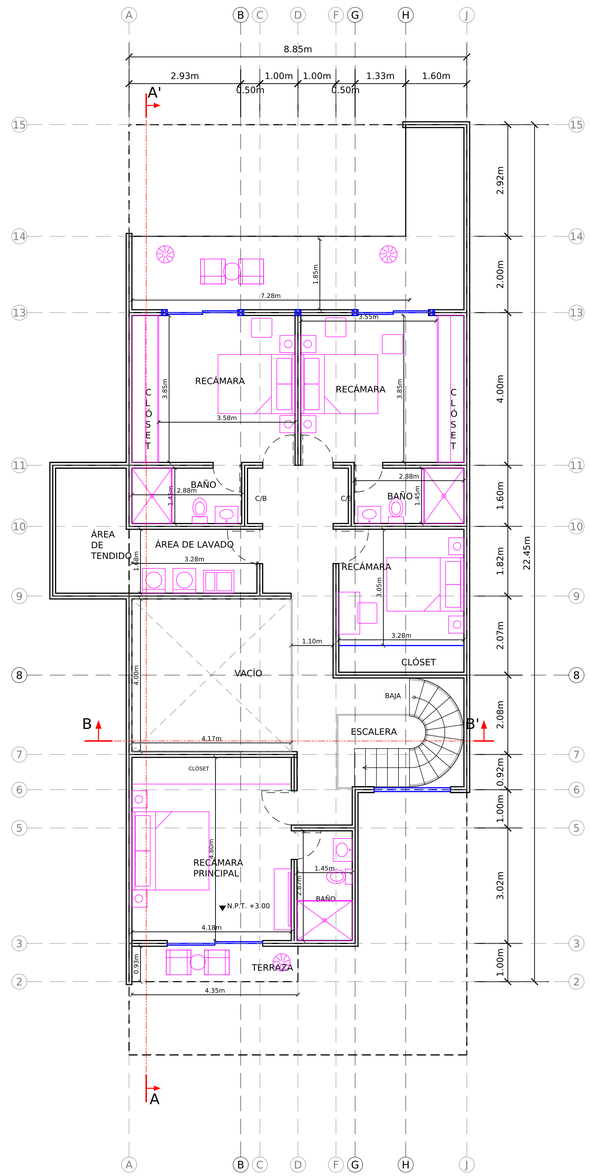

PLANTA PRIMER NIVEL

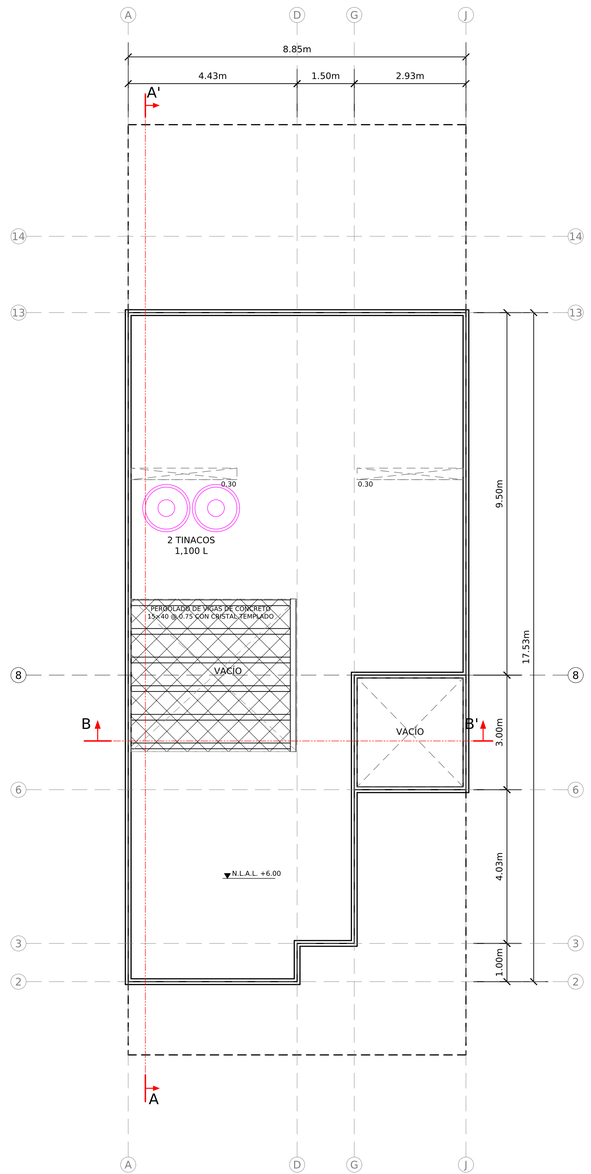

PLANTA DE AZOTEA

NOTAS DE CORTES

1. COTAS Y NIVELES EN METROS; NIVELES REFERIDOS AL N.P.T. DE PLANTA BAJA (±0.00).
2. ENTREPISO: LOSA ALIGERADA DE CASETONES 60×60×20 CON NERVADURAS DE 10 cm Y CAPA DE 5 cm (h = 0.25); MACIZADA EN APOYOS.
3. AZOTEA: LOSA ALIGERADA RETICULAR, MISMO SISTEMA QUE EL ENTREPISO (PERALTE FINAL SEGÚN CÁLCULO ESTRUCTURAL). SOBRE EL VACÍO: VIGAS DE CONCRETO 15×40 @ 0.75 CON CRISTAL TEMPLADO.
4. ALTURAS PROPUESTAS: ENTREPISO 3.00; PUERTAS 2.10; VENTANAS 0.90 A 2.10; PRETIL AZOTEA 0.60; PRETIL TERRAZAS 1.00.
5. PUERTAS: EL VANO INCLUYE EL ESPESOR DE LA HOJA (EJ. PUERTA DE 0.75 = HOJA 0.70 + 0.05).
6. ESCALERA CURVA SIN EL PRIMER ESCALÓN ORIGINAL: 17 PERALTES DE 0.1765 Y 16 HUELLAS EN U: 5 RECTAS DE 0.29 + 11 RADIALES DE 0.264 EN LÍNEA DE HUELLA (MÍN. 0.25). VER LÁMINA A-03.
7. FIGURAS HUMANAS, VEGETACIÓN, VEHÍCULOS Y MOBILIARIO: REFERENCIA DE ESCALA.

SIMBOLOGÍA


- MURO CORTADO
- CONCRETO CORTADO (LOSA, NERVADURA, TRABE, ESCALERA)
- CASETÓN DE POLIESTIRENO
- MURO DE PIEDRA (VISTO)
- TERRENO NATURAL / RELLENO

REVISIONES
R1.5 SEP-2026 EMISIÓN ANTERIOR.
R1.6 OCT-2026 COMEDOR PARA 15 PERSONAS; ESCALERA SIN EL PRIMER ESCALÓN (17 PERALTES, HUELLAS EN U); EJES H Y 10 A CENTRO DE MURO; MURO, PUERTA Y MUEBLE EN RECÁMARA PRINCIPAL; BLOQUES DE AUTOS Y SALA; COTAS Y NOTAS SIN ENCIMARSE; DIBUJOS AMPLIADOS EN LÁMINAS.

CASA HABITACIÓN «CROCHA»


PLANTAS ARQUITECTÓNICAS

ESCALA: 1:75 / NOTAS 1:50	ACOTACIONES: METROS
FECHA: OCTUBRE 2026 DIBUJÓ: ARCHIVO: 001_PLANO_CROCHA_R1.7.dxf	CLAVE: A-01 REVISÓ:

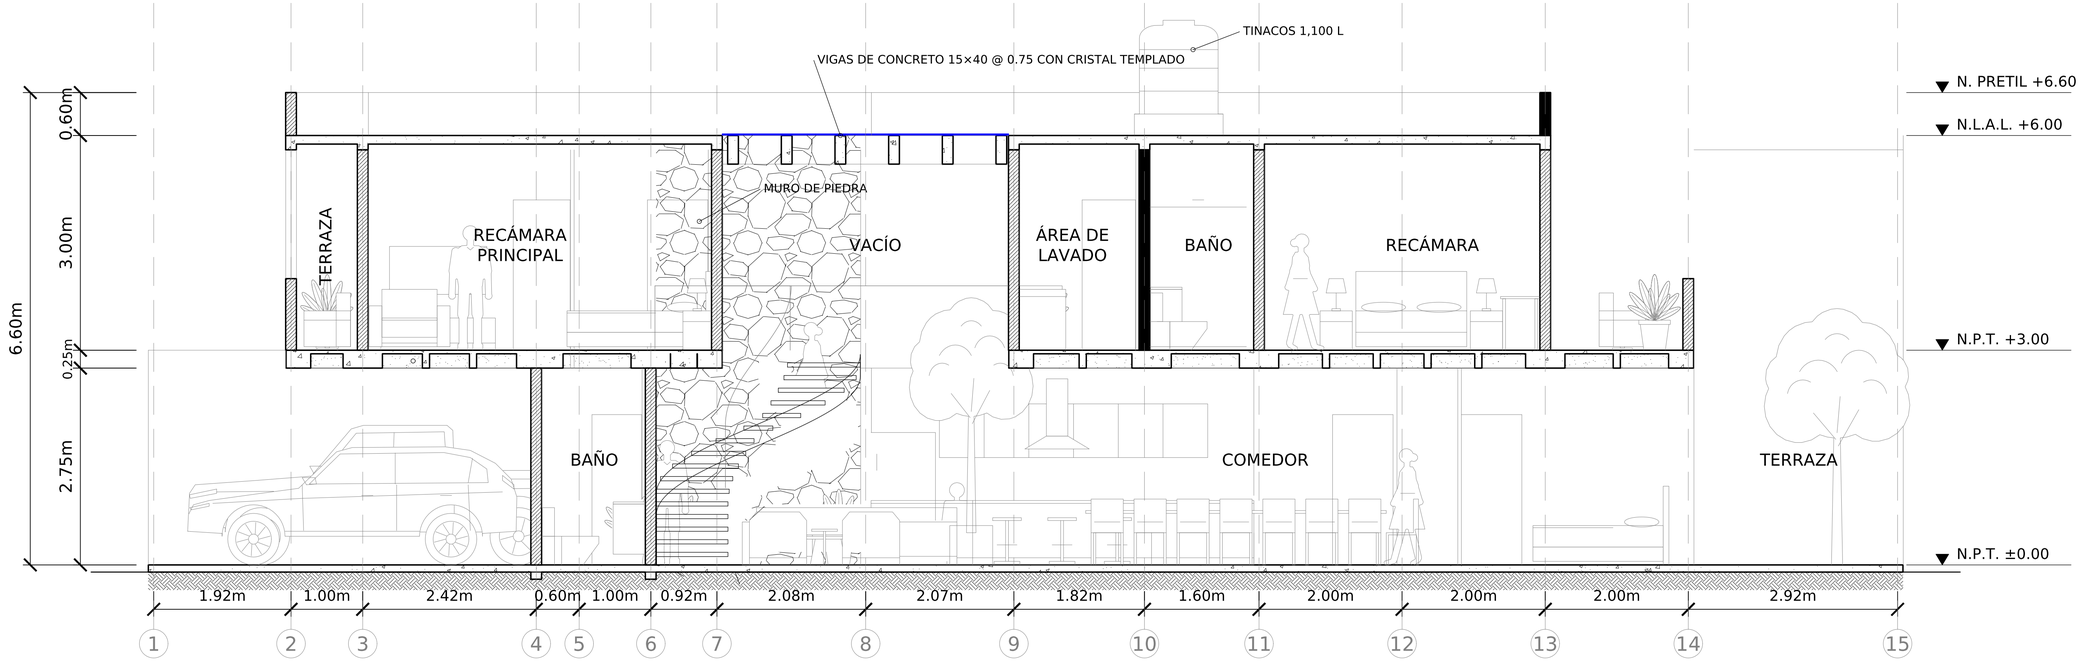

CORTE A-A'

LONGITUDINAL (VISTA HACIA EJE J)

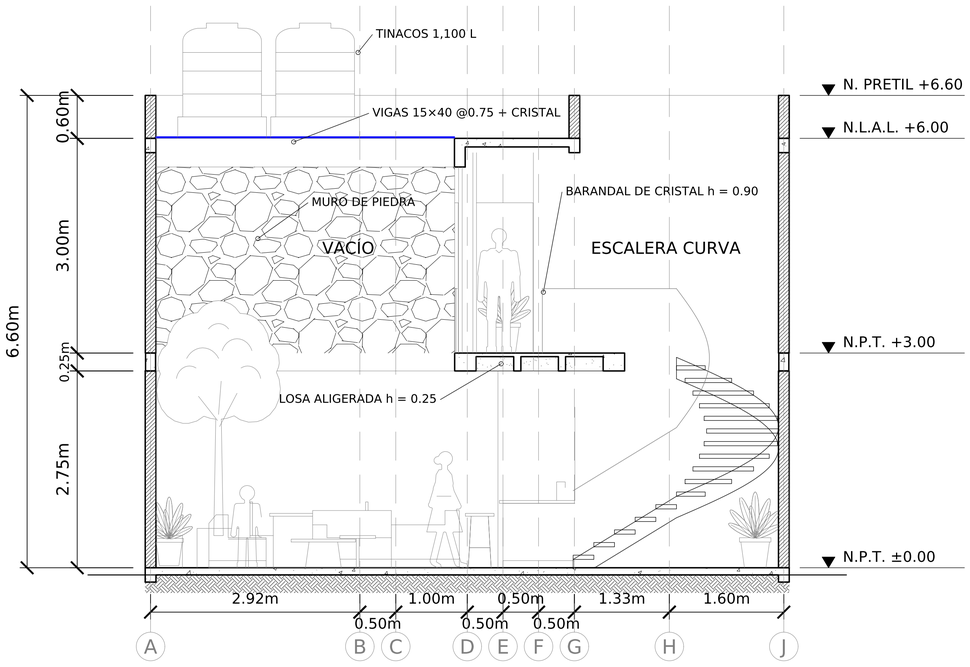

CORTE B-B'

TRANSVERSAL (VISTA HACIA EJE 15)

NOTAS DE CORTES

1. COTAS Y NIVELES EN METROS; NIVELES REFERIDOS AL N.P.T. DE PLANTA BAJA (±0.00).
2. ENTREPISO: LOSA ALIGERADA DE CASETONES 60×60×20 CON NERVADURAS DE 10 cm Y CAPA DE 5 cm (h = 0.25); MACIZADA EN APOYOS.
3. AZOTEA: LOSA ALIGERADA RETICULAR, MISMO SISTEMA QUE EL ENTREPISO (PERALTE FINAL SEGÚN CÁLCULO ESTRUCTURAL). SOBRE EL VACÍO: VIGAS DE CONCRETO 15×40 @ 0.75 CON CRISTAL TEMPLADO.
4. ALTURAS PROPUESTAS: ENTREPISO 3.00; PUERTAS 2.10; VENTANAS 0.90 A 2.10; PRETIL AZOTEA 0.60; PRETIL TERRAZAS 1.00.
5. PUERTAS: EL VANO INCLUYE EL ESPESOR DE LA HOJA (EJ. PUERTA DE 0.75 = HOJA 0.70 + 0.05).
6. ESCALERA CURVA SIN EL PRIMER ESCALÓN ORIGINAL: 17 PERALTES DE 0.1765 Y 16 HUELLAS EN U: 5 RECTAS DE 0.29 + 11 RADIALES DE 0.264 EN LÍNEA DE HUELLA (MÍN. 0.25). VER LÁMINA A-03.
7. FIGURAS HUMANAS, VEGETACIÓN, VEHÍCULOS Y MOBILIARIO: REFERENCIA DE ESCALA.


SIMBOLOGÍA

- MURO CORTADO
- CONCRETO CORTADO (LOSA, NERVADURA, TRABE, ESCALERA)
- CASETÓN DE POLIESTIRENO
- MURO DE PIEDRA (VISTO)
- TERRENO NATURAL / RELLENO

REVISIONES
R1.5 SEP-2026 EMISIÓN ANTERIOR.
R1.6 OCT-2026 COMEDOR PARA 15 PERSONAS; ESCALERA SIN EL PRIMER ESCALÓN (17 PERALTES, HUELLAS EN U); EJES H Y 10 A CENTRO DE MURO; MURO, PUERTA Y MUEBLE EN RECÁMARA PRINCIPAL; BLOQUES DE AUTOS Y SALA; COTAS Y NOTAS SIN ENCIMARSE; DIBUJOS AMPLIADOS EN LÁMINAS.


CASA HABITACIÓN «CROCHA»	
CORTES ARQUITECTÓNICOS	
ESCALA: 1:40 / NOTAS 1:50	ACOTACIONES: METROS
FECHA: OCTUBRE 2026 DIBUJÓ: ARCHIVO: 001_PLANO_CROCHA_R1.7.dxf	CLAVE: A-02 REVISÓ:

ESCALERA CURVA — DETALLE (RECALCULADA: SE ELIMINA EL PRIMER ESCALÓN)

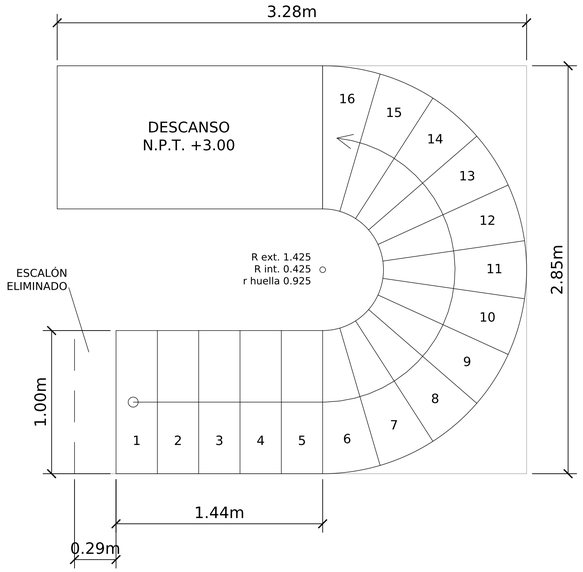


PLANTA

ESC. 1:20

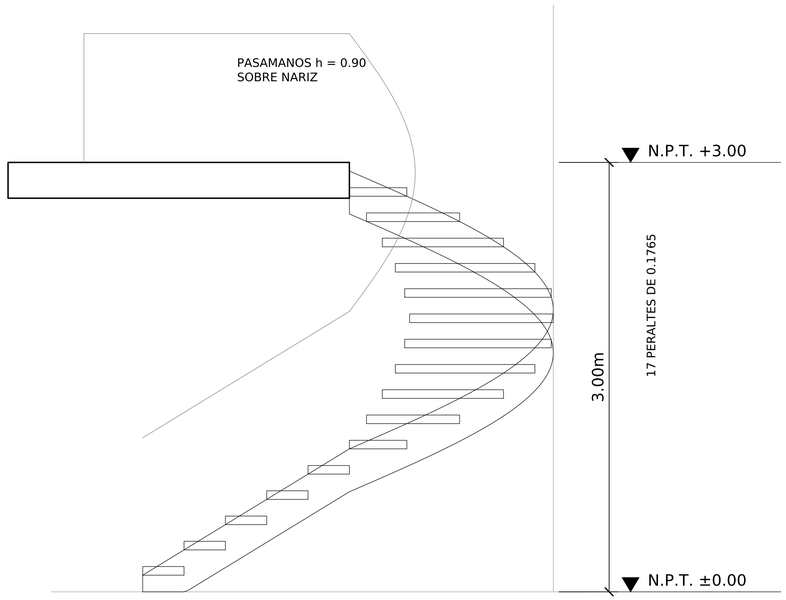

ALZADO (VISTA HACIA EJE 15)

ESC. 1:20

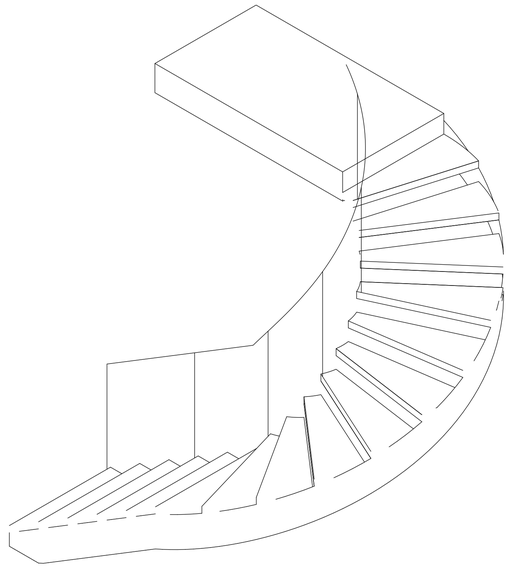

ISOMÉTRICO (SIN ESCALA)

TABLA 1. GEOMETRÍA POR PELDAÑO (m)

PE-RALTE	NIVEL HUELLA	HUELLA EN LÍNEA DE HUELLA	HUELLA A 0.40 DEL BARANDAL INT.	HUELLA BORDE INT.	HUELLA BORDE EXT.
1	0.176	0.289	0.289	0.289	0.289
2	0.353	0.289	0.289	0.289	0.289
3	0.529	0.289	0.289	0.289	0.289
4	0.706	0.289	0.289	0.289	0.289
5	0.882	0.289	0.289	0.289	0.289
6	1.059	0.264	0.236	0.121	0.407
7	1.235	0.264	0.236	0.121	0.407
8	1.412	0.264	0.236	0.121	0.407
9	1.588	0.264	0.236	0.121	0.407
10	1.765	0.264	0.236	0.121	0.407
11	1.941	0.264	0.236	0.121	0.407
12	2.118	0.264	0.236	0.121	0.407
13	2.294	0.264	0.236	0.121	0.407
14	2.471	0.264	0.236	0.121	0.407
15	2.647	0.264	0.236	0.121	0.407
16	2.824	0.264	0.236	0.121	0.407
17	3.000	LLEGADA	N.P.T.	+3.00	—

TABLA 2. TRAZO DE NARICES (m, ORIGEN EN EL CENTRO DEL GIRO)

NARIZ	INT. X	INT. Y	EXT. X	EXT. Y
0	-1.444	-0.425	-1.444	-1.425
1	-1.155	-0.425	-1.155	-1.425
2	-0.866	-0.425	-0.866	-1.425
3	-0.578	-0.425	-0.578	-1.425
4	-0.289	-0.425	-0.289	-1.425
5	0.000	-0.425	0.000	-1.425
6	0.120	-0.408	0.401	-1.367
7	0.230	-0.358	0.770	-1.199
8	0.321	-0.278	1.077	-0.933
9	0.387	-0.177	1.296	-0.592
10	0.421	-0.060	1.410	-0.203
11	0.421	0.060	1.410	0.203
12	0.387	0.177	1.296	0.592
13	0.321	0.278	1.077	0.933
14	0.230	0.358	0.770	1.199
15	0.120	0.408	0.401	1.367
16	0.000	0.425	0.000	1.425

NOTAS DE LA ESCALERA

1. SE ELIMINA EL PRIMER ESCALÓN: EL ARRANQUE SE RECORRE 0.29 m (DE 37.551 A 37.841 EN EJES DE PLANTA).
2. DESNIVEL 3.00 m = 17 PERALTES DE 0.1765 m (MÁX. 0.18 ✓).
3. FORMA DE U: 5 HUELLAS RECTAS + 11 RADIALES EN EL MEDIO GIRO. EN LÍNEA DE HUELLA (r = 0.925) 0.264 A 0.289 m (MÍN. 0.25 ✓); A 0.40 m DEL BARANDAL INTERIOR 0.236 A 0.289 m.
4. 2P + H = 0.617 A 0.642 m (ENTRE 0.61 Y 0.65 ✓).
5. HUELLA MÍNIMA 0.25 MEDIDA EN LÍNEA DE HUELLA; CON 16 PERALTES EL PERALTE SERÍA 0.1875 m (NO CUMPLE), POR ESO SE CONSERVAN 17.
6. TRAZO: TRAMO RECTO CON NARICES PERPENDICULARES; EN EL GIRO, NARICES RADIALES AL CENTRO (TABLA 2).
7. ANCHO 1.00 m; R EXT. 1.425; R INT. 0.425. HUELLAS e = 0.06 SOBRE ZANCA CURVA EXTERIOR; BARANDAL DE CRISTAL TEMPLADO h = 0.90.
8. VERIFICAR CON EL D.R.O.: EL REGLAMENTO DE MORELIA PIDE HUELLA 0.28 Y MÁX. 15 PERALTES ENTRE DESCANSOS (LA ESCALERA ORIGINAL YA TENÍA 17).

REVISIONES
R1.5 SEP-2026 EMISIÓN ANTERIOR.
R1.6 OCT-2026 COMEDOR PARA 15 PERSONAS; ESCALERA SIN EL PRIMER ESCALÓN (17 PERALTES, HUELLAS EN U); EJES H Y 10 A CENTRO DE MURO; MURO, PUERTA Y MUEBLE EN RECÁMARA PRINCIPAL; BLOQUES DE AUTOS Y SALA; COTAS Y NOTAS SIN ENCIMARSE; DIBUJOS AMPLIADOS EN LÁMINAS.

CASA HABITACIÓN «CROCHA»

ESCALERA CURVA — DETALLE

ESCALA: 1:20	ACOTACIONES: METROS
FECHA: OCTUBRE 2026 DIBUJÓ: ARCHIVO: 001_PLANO_CROCHA_R1.7.dxf	CLAVE: A-03 REVISÓ: